

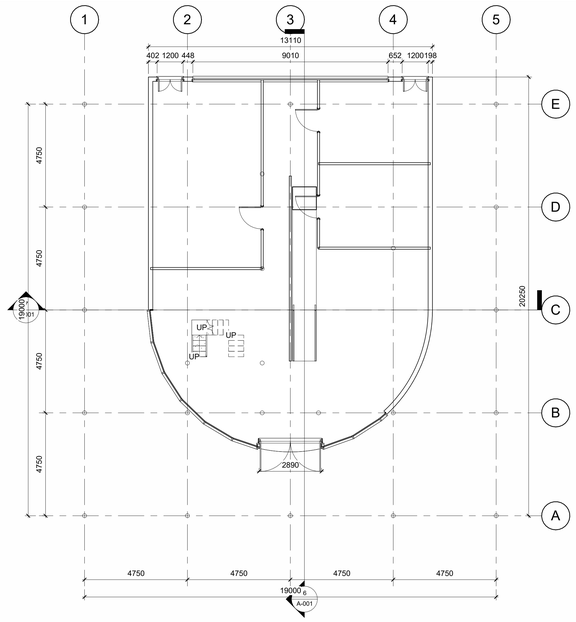



1 PLAN - GROUND (+0.00)
1 : 100

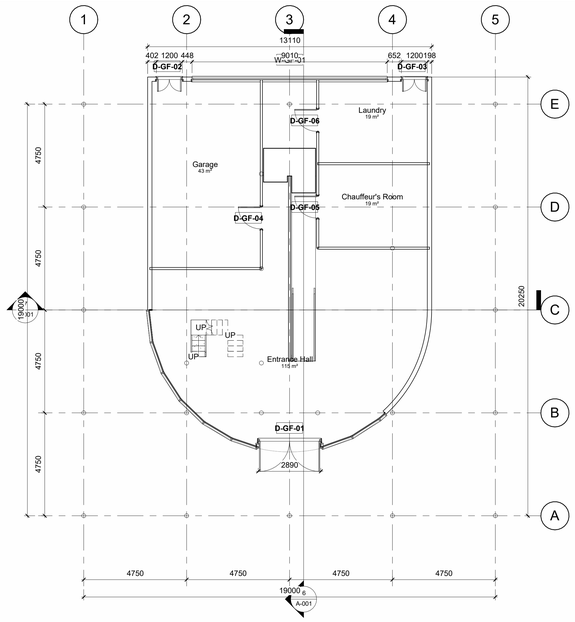


2 PLAN - GROUND FLOOR (+0.15)
1 : 100

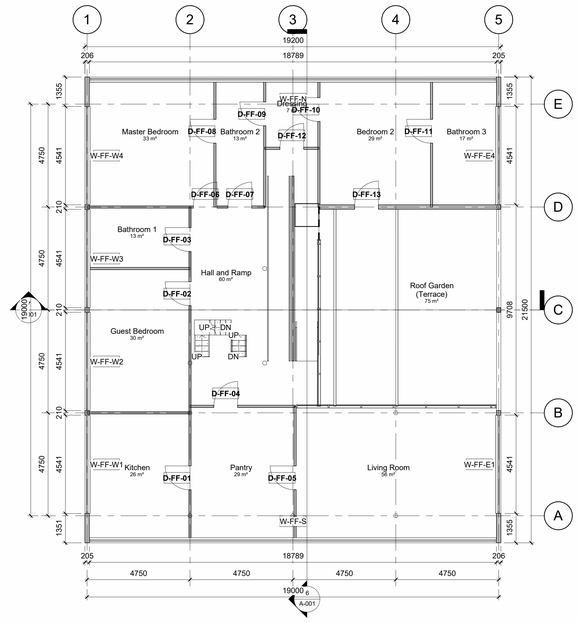


3 PLAN - FIRST FLOOR (+3.45)
1 : 100

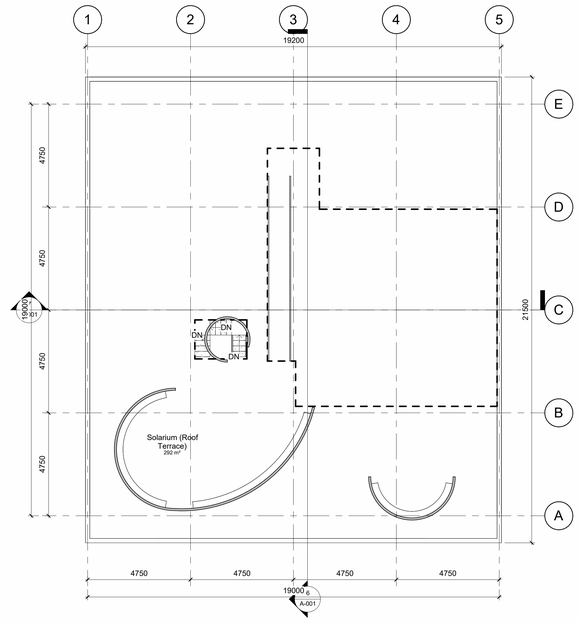


4 PLAN - ROOF TERRACE (+6.75)
1 : 100

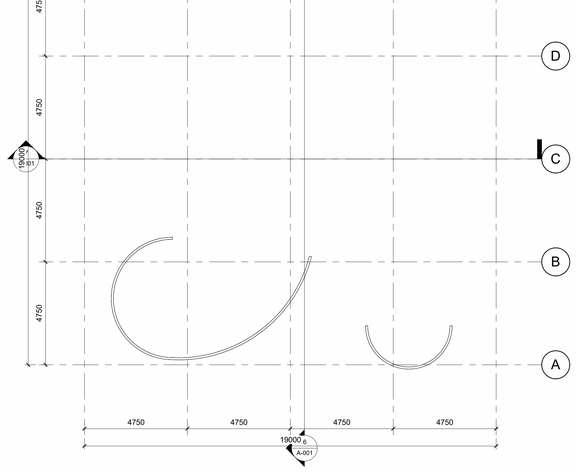


5 PLAN - SOLARIUM TOP (+9.45)
1 : 100

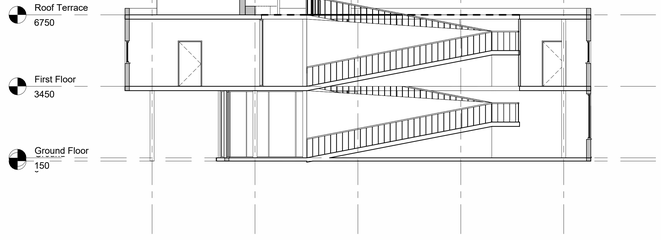

6 SECTION A-A - LONGITUDINAL ALONG RAMP
1 : 100

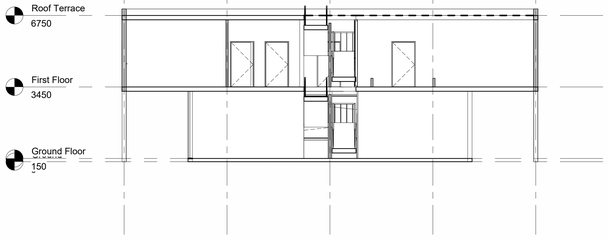

7 SECTION B-B - CROSS SECTION ON GRID C
1 : 100

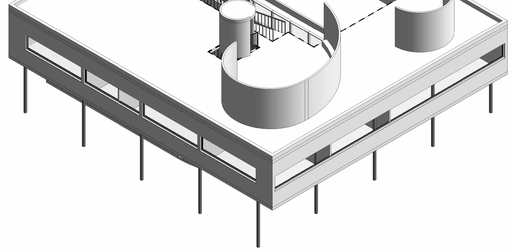


8 3D AXONOMETRIC VIEW FROM SOUTH-WEST


PROJECT: VILLA SAVOYE - Poissy (Le Corbusier, 1931)

General Arrangement - Plans, Sections A-A / B-B, Elevations, 3D axonometric


SHEET No. A-001 BIM model (Revit) - 2026-10-27 - Units mm - Levels: Ground 0 / GF +150 / FF +3450 / RT +6750 / ST +9450	SCALE 1:100	SIZE A0 landscape

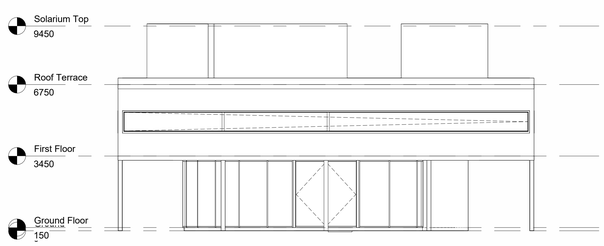


9 SOUTH ELEVATION (ENTRANCE)
1 : 100

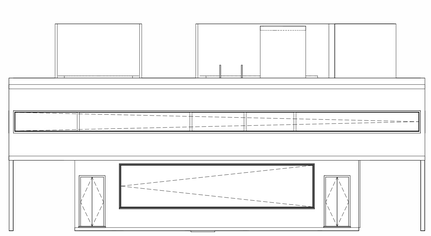

10 NORTH ELEVATION
1 : 100

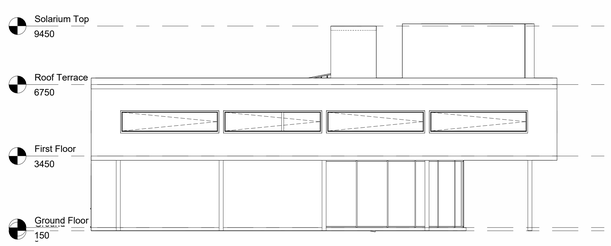

11 WEST ELEVATION
1 : 100

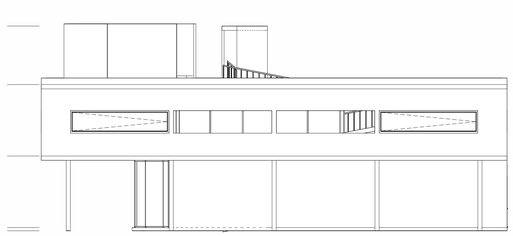

12 EAST ELEVATION
1 : 100